
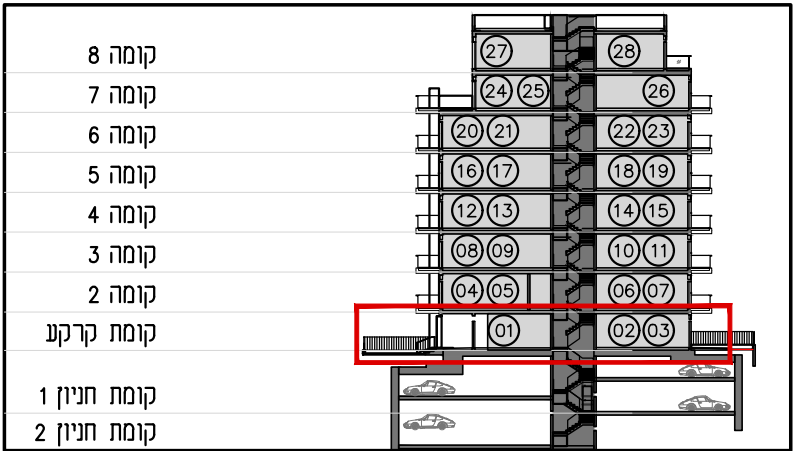
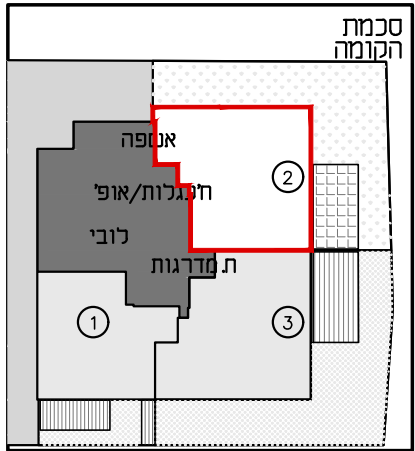


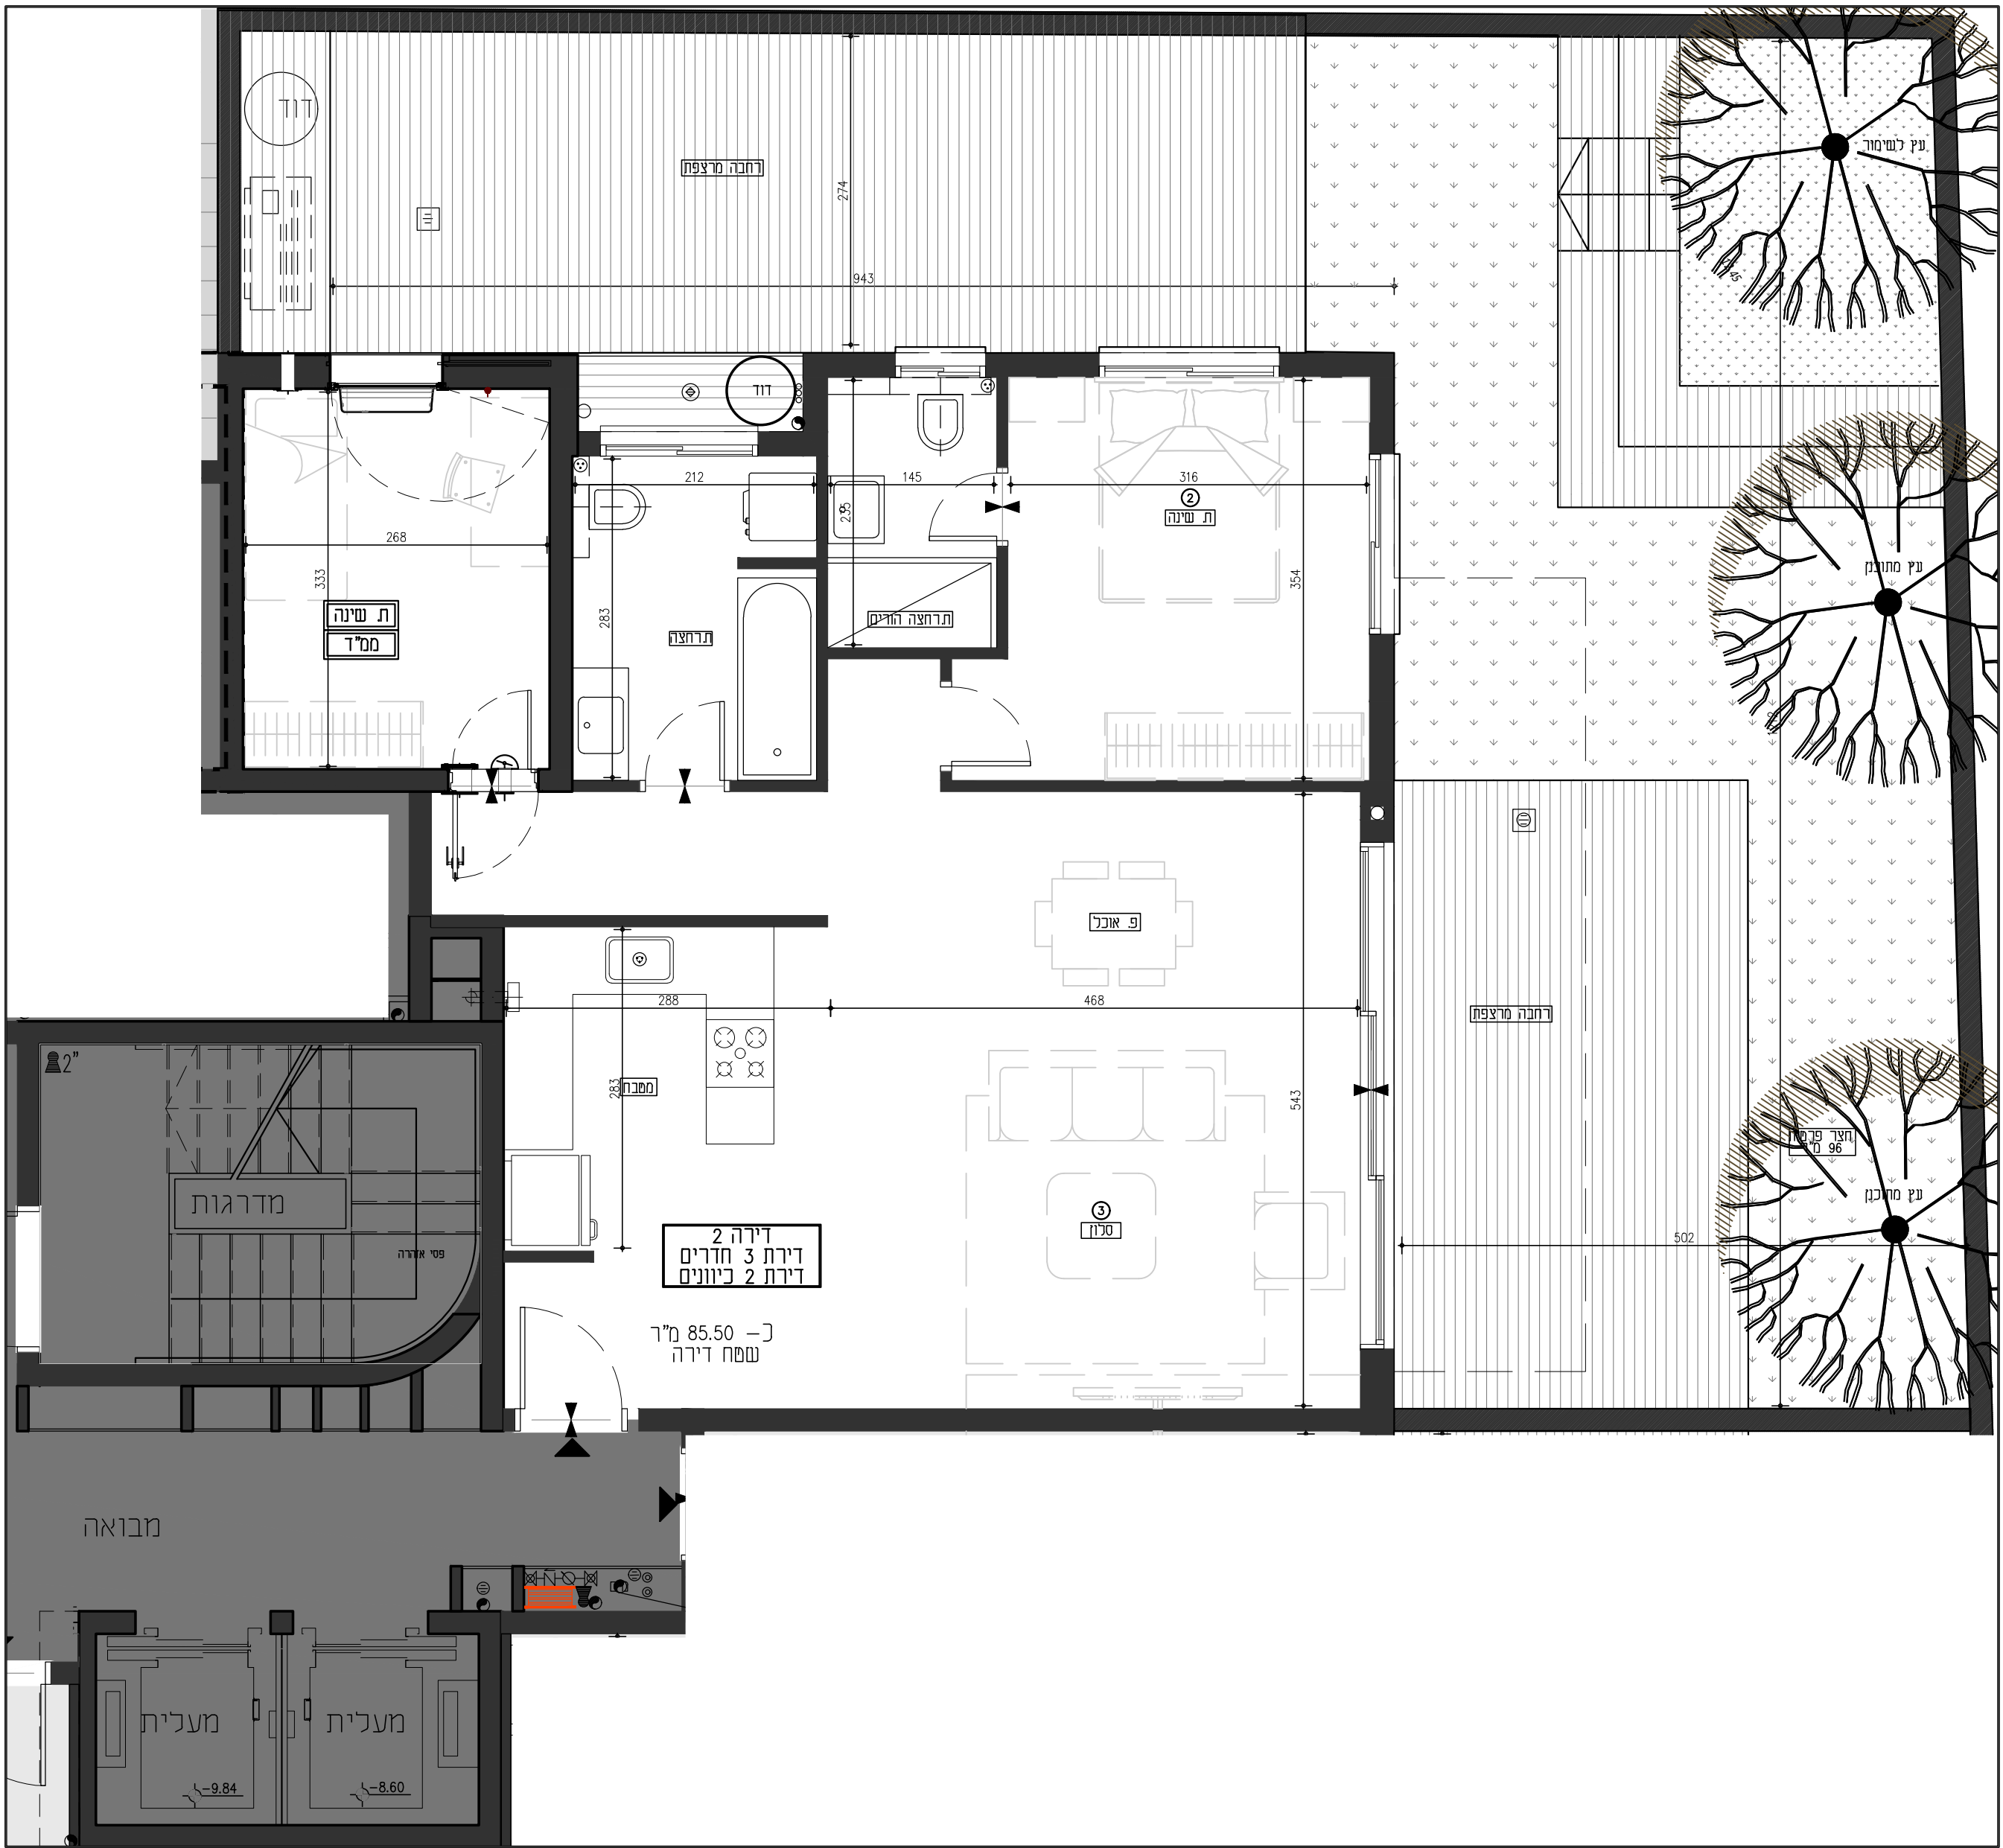

מקרא לתכניות מפר			
סימון שטח משותף (כולל פירים)	סימון שטח משותף (כולל פירים)	סימון שטח משותף (כולל פירים)	סימון שטח משותף (כולל פירים)
סימון תוספת בנייה בדירות קיימות / לדירות א-זוגיות בקומות החדשות	סימון תוספת בנייה בדירות קיימות / לדירות א-זוגיות בקומות החדשות	סימון תוספת בנייה בדירות קיימות / לדירות א-זוגיות בקומות החדשות	סימון תוספת בנייה בדירות קיימות / לדירות א-זוגיות בקומות החדשות
סימון לשטח מערכות משותף קרקע/גג	סימון לשטח מערכות משותף קרקע/גג	סימון לשטח מערכות משותף קרקע/גג	סימון לשטח מערכות משותף קרקע/גג
סימון לגינה פרטית	סימון לגינה פרטית	סימון לגינה פרטית	סימון לגינה פרטית
סימון לגינה משותפת	סימון לגינה משותפת	סימון לגינה משותפת	סימון לגינה משותפת
סימון לרחבה מרוצפת בחצר פרטית	סימון לרחבה מרוצפת בחצר פרטית	סימון לרחבה מרוצפת בחצר פרטית	סימון לרחבה מרוצפת בחצר פרטית
סימון למרפסת	סימון למרפסת	סימון למרפסת	סימון למרפסת
קיר קיים	קיר קיים	קיר קיים	קיר קיים
קיר / עמוד בטון חדש	קיר / עמוד בטון חדש	קיר / עמוד בטון חדש	קיר / עמוד בטון חדש
פיר - חלל / פתח ברצפה	פיר - חלל / פתח ברצפה	פיר - חלל / פתח ברצפה	פיר - חלל / פתח ברצפה

מחזור: 5	תאריך: 11/12/2022	קנ"מ: 1:50	מוזיר יעקב 8, תל-אביב
תכניות מפר	תכנית קומת קרקע, דירה 2	ראה הערות כלליות בתחילת חוברת זו	

מוזיר 8 ת"א בע"מ

חומה ומגדל 26, תל אביב
ט: 072-2818121 :9 072-2727711